
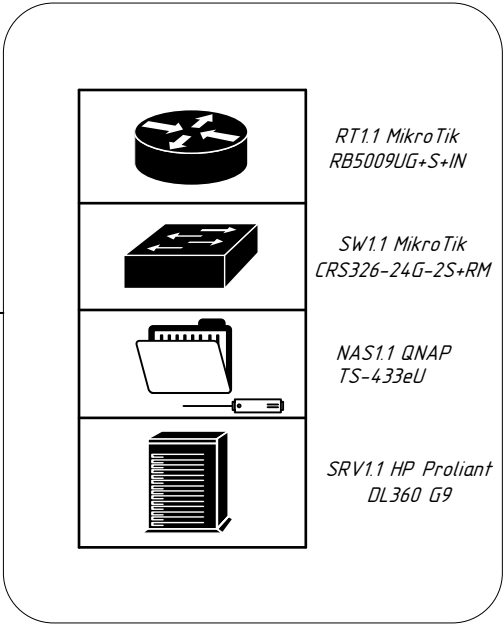


Первый этаж

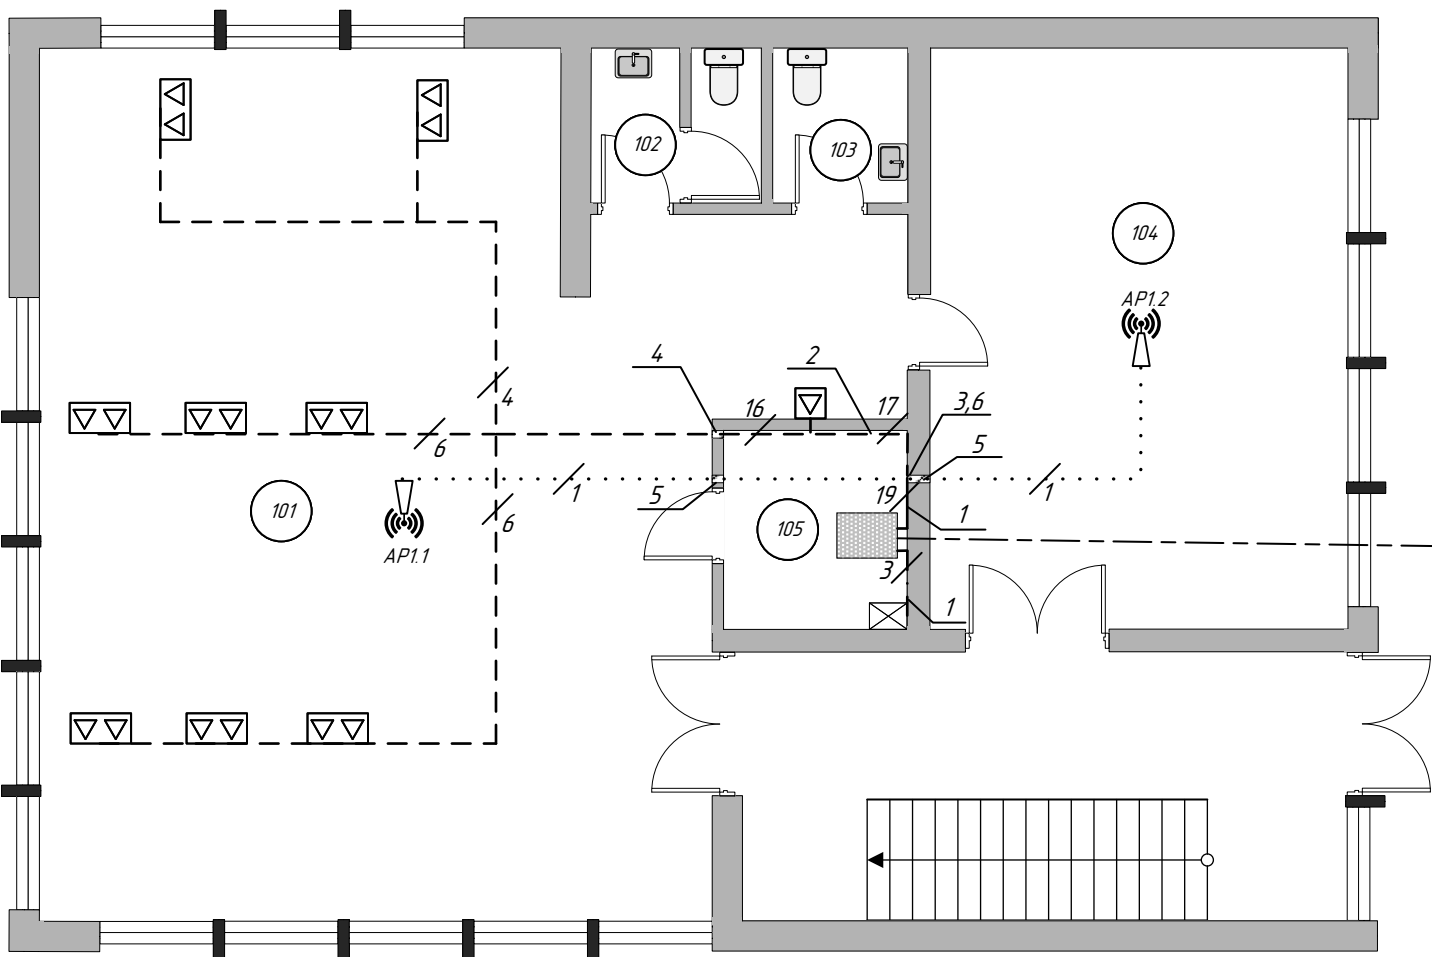

Технические требования:

Кабель прокладывается в кабель-канале под полом, над фальшпотолком и вдоль стены на расстоянии 20 см от пола.

Информационные розетки на всех этажах располагаются в напольных люках.

Шкаф ставится на пол в серверной комнате.

Точки доступа монтируются к фальшпотолку. Необходимо использовать специальную металлическую монтажную пластину, которая устанавливается сверху плиты, а снизу к ней крепится пластина из комплекта точки доступа, для это просверлить отверстия для шурупов. Необходимо сделать отверстие в фальшпанели для кабеля, пропустить его через него, подключить к точке доступа, а затем зафиксировать ее на пластине.

1. Кабель располагается вдоль стены на расстояние 20 см от пола.
2. Кабель располагается в полу.
3. Кабель располагается над фальшпотолком.
4. В данном месте кабель пускается в канал смонтированный под стеной.
5. В данном месте кабель пускается в канал смонтированный над фальшпотолком через стену.
6. Кабель опускается/поднимается вертикально по стене.

Условные обозначения					
	Информационная розетка RJ45 для стационарного подключения		Стальная балка		Витая пара в кабель канале в полу
	Двойная информационная розетка RJ45 для стационарного подключения		Панорамное остекление		Витая пара в гофрированной трубе над фальшпотолком
	Телекоммуникационный шкаф		Кабельная шахта		Витая пара в кабель канале
	Железобетонная стена		Номер помещения		Два патч-корда Cat6, 15 метров + одно оптоволокно в кабель канале
	Кирпичная стена		Беспроводная точка доступа		Комментарий

					ГЧИР.400201.021 СЗ					
					Локальная компьютерная сеть. План здания	Лит.		Масса	Масштаб	
Изм.	Лист	№ докум.	Подп.	Дата			У		1:100	
Разраб.		Николайчик								
Пров.		Глецевич								
Т. контр.										
Реценз.						Лист		1	Листов	2
Н. контр.						ЭВМ, гр. 250501				
Утв.										