
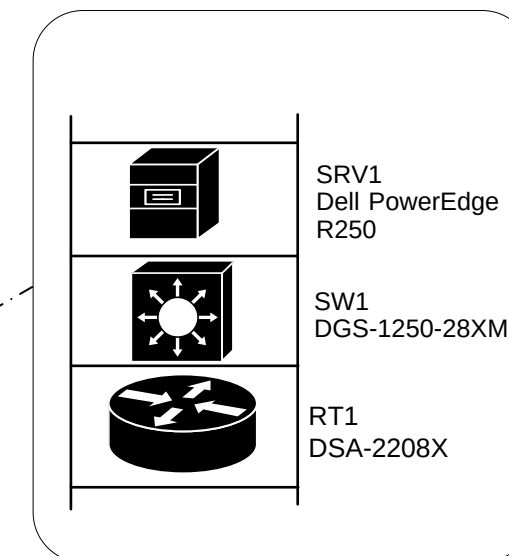


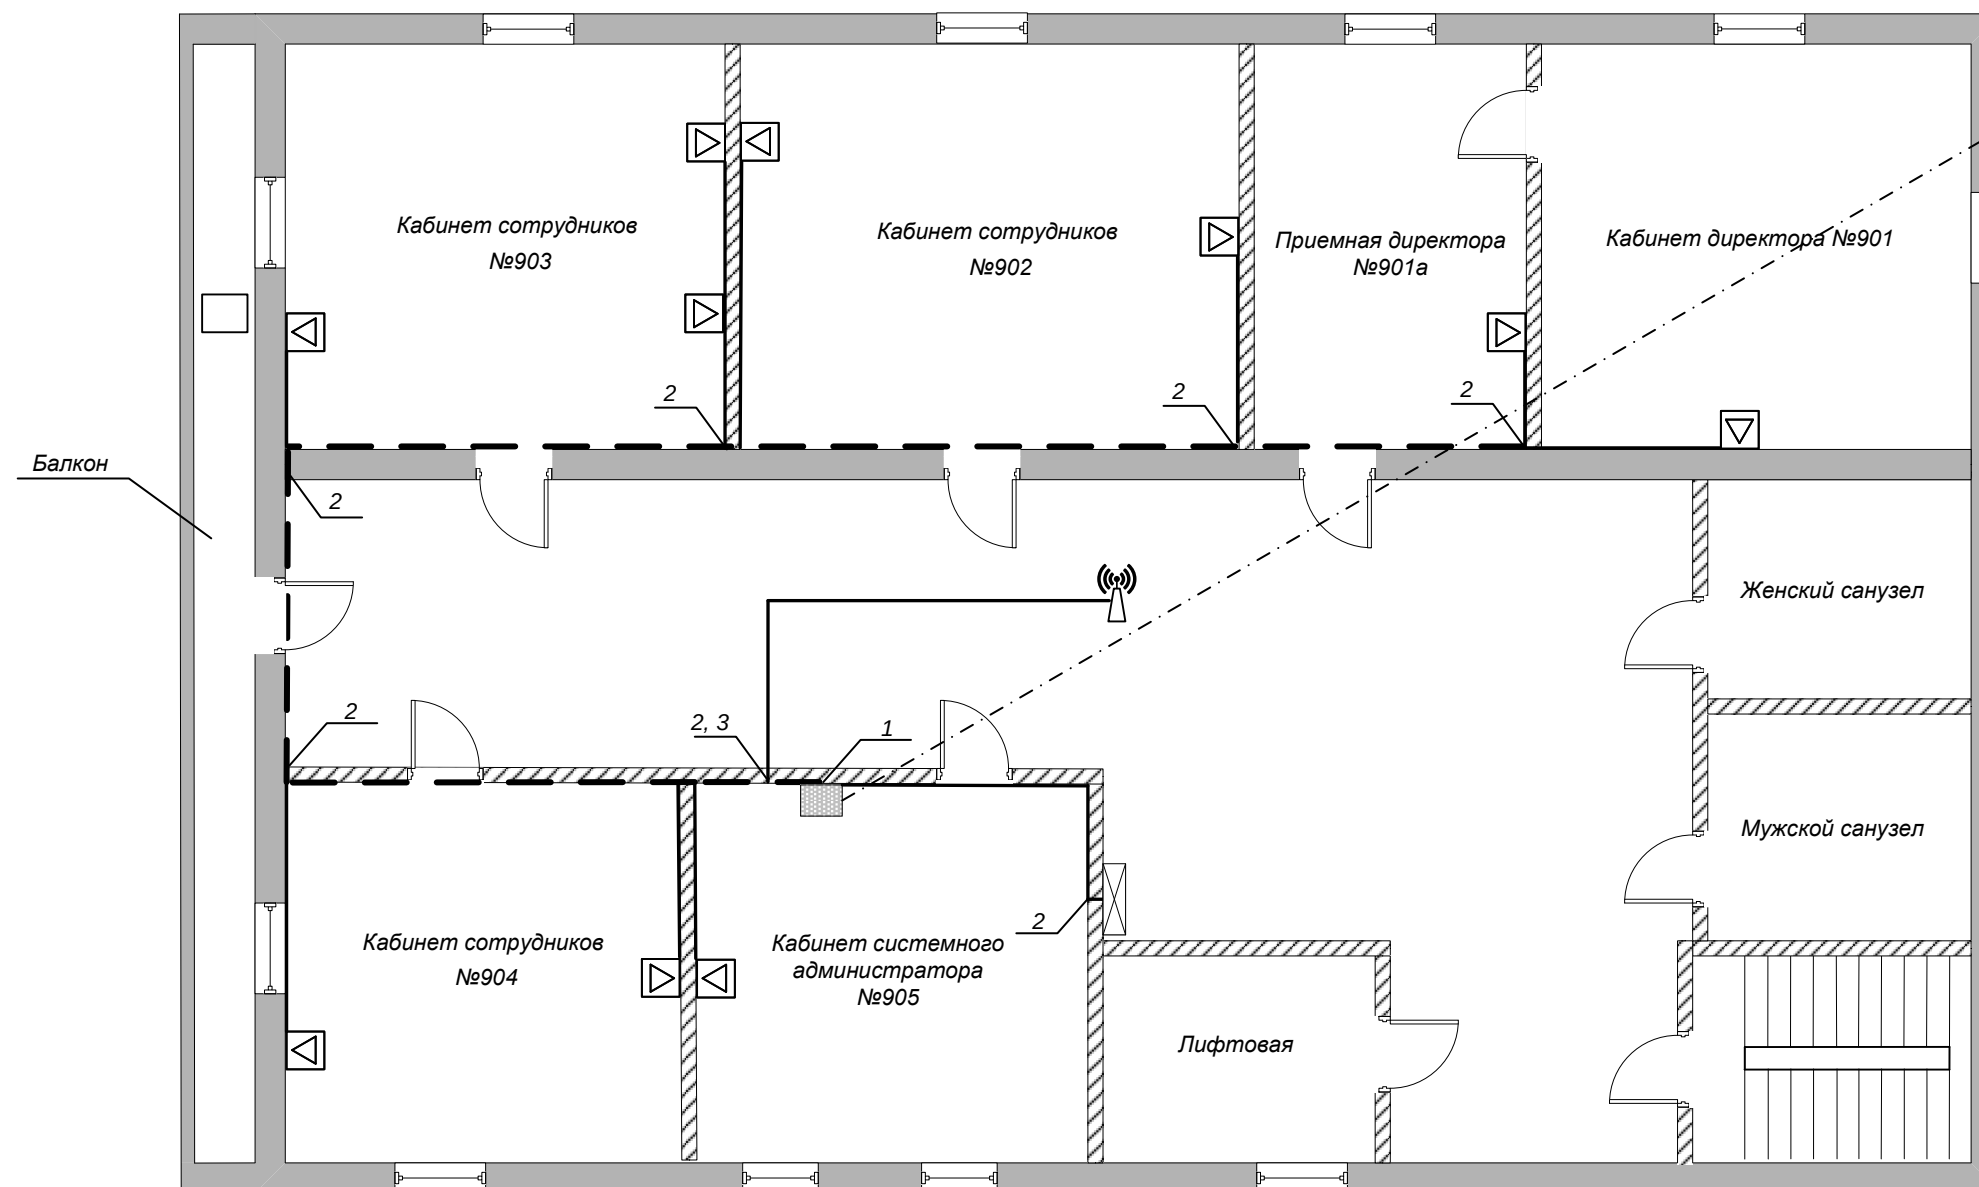

Технические требования:

Кабель везде прокладывается в кабель-канале
вдоль стены на расстоянии 30 см от потолка.

Информационные розетки на всех этажах располагаются на высоте 50 см от уровня пола. Кабель опускается вертикально вниз в таких местах.

Шкаф крепится к стене на высоте 150 см от уровня пола.

Точки доступа монтируются к потолку.

1) Кабель поднимается вверх вдоль стены на расстояние 30 см от потолка.

2) В данном месте для дальнейшей прокладки кабеля сверлится отверстие в стене и через него проводится кабель.

3) Кабель проводится над фальшь-потолком.

Условные обозначения



Информационная розетка
PST00 39047



Телекоммуникационный
шкаф настенный ШТВ-Н-
18.6.5-КААА-ТК




Железобетонная стена



Газосиликатная стена



Кабельная шахта

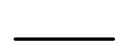

*Витая пара в кабель-
канале 15x10*

Витая пара в кабель-
канале 40x15



Противопожарный
эвакуационный люк с
лестницей



Маршрутизатор



L3-коммутатор



Беспроводная точка доступа



Файловый сервер

					ГУИР.400201.012 СЗ				
					Локальная компьютерная сеть План здания	Лит.	Масса	Масштаб	
Изм.	Лист	№ докум.	Подп.	Дата		у		1:75	
Разраб.	Ковальчук								
Пров.	Глецевич								
Т. контр.						Лист	Листов	1	
Реценз.						ЭВМ, гр. 150501			
Н. контр.									
Утв.									