



План 1 этажа

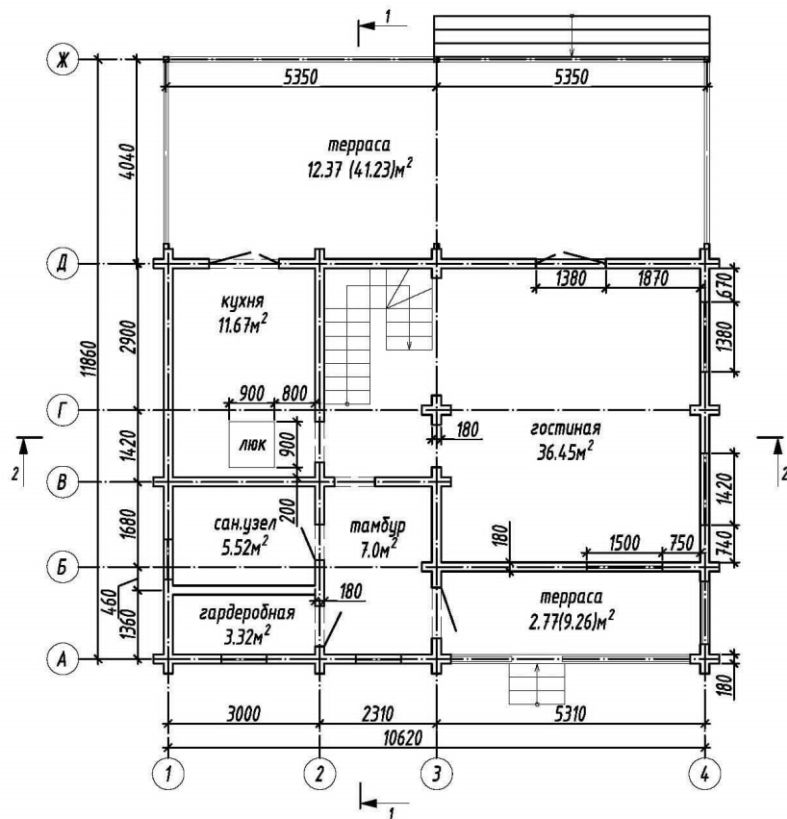

1. Разрез 1-1 см.л. 10.
2. Разрез 2-2 см.л. 11.

Инв.№ подл.	Подп. и дата	Взаим.инв.№					
		Изм.	Кол.ч.	Лист	Ндоп.	Подп.	Дата
	ГИП	Кухмар					12.20
	Разраб.	Кухмар					12.20
	Н.контр.	Кухмар					12.20
Строительство жилого дома на земельном участке площадью 0,1479 га по адресу: Минский р-н, Колодищанский с/с, п. Колодищи, ул. Алеся Адамовича,							
Частный жилой дом						Стадия	Лист
						С	6
План 1 этажа						ИП Кухмар Д.А. Свидетельство о регистрации №192530811 Аттестаты соответствия ИАЭС №0001934-ГР, №0002091-ГР до 05.12.2021	


Разрез 1-1

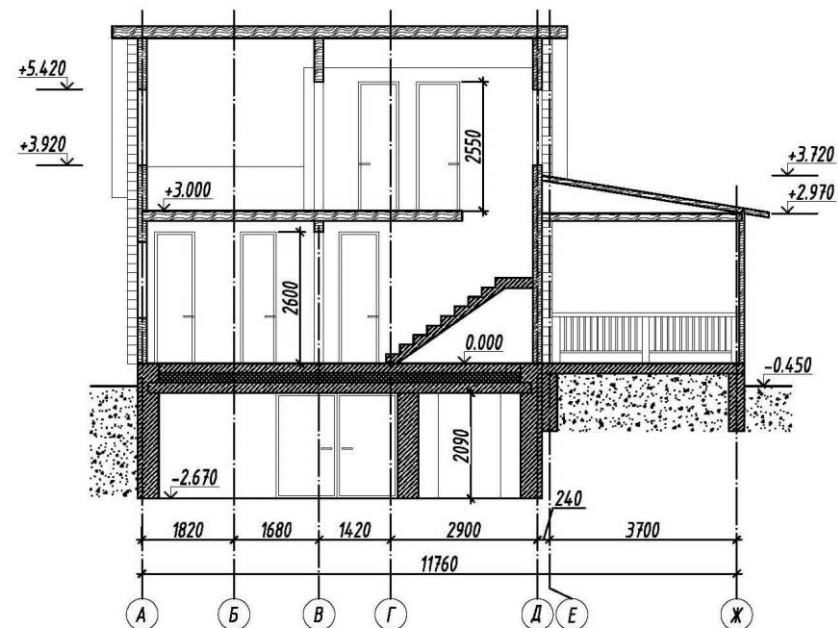

1. План 1 этажа дома см.л. 6;
2. План мансардного этажа см.л. 7;
3. План подвального этажа см.л. 8.

Инв.№ подл.	Подп. и дата	Взаим.инв.№					
		Изм.	Кол.ч.	Лист	Ндоп.	Подп.	Дата
	ГИП	Кухмар					12.20
	Разраб.	Кухмар					12.20
	Н.контр.	Кухмар					12.20
Строительство жилого дома на земельном участке площадью 0,1479 га по адресу: Минский р-н, Колодищанский с/с, п. Колодищи, ул. Алеся Адамовича,							
Частный жилой дом						Стадия	Лист
						С	10
Разрез 1-1						ИП Кухмар Д.А. Свидетельство о регистрации №192530811 Аттестаты соответствия ИАЭС №0001934-ГР, №0002091-ГР до 05.12.2021	

Разрез 2-2

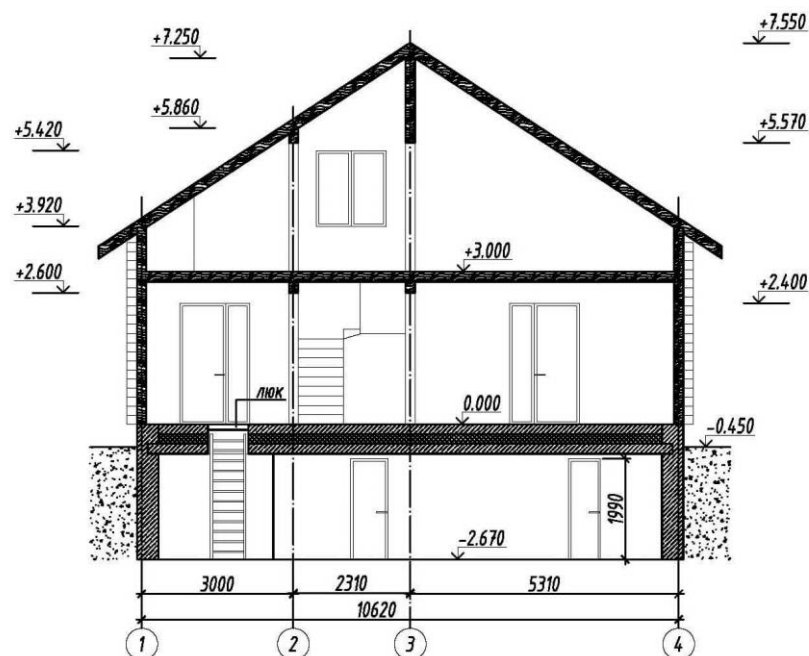

1. План 1 этажа дома см.л. 6;
2. План мансардного этажа см.л. 7;
3. План подвального этажа см.л. 8.

Взаим.инв.№		1. План 1 этажа дома см.л. 6; 2. План мансардного этажа см.л. 7; 3. План подвального этажа см.л. 8.									
								Строительство жилого дома на земельном участке площадью 0,1479 га по адресу: Минский р-н, Колодищанский с/с, п. Колодищи, ул. Алеся Адамовича,			
Подп. и дата		Изм.	Кол.ч.	Лист	Ндок.	Подп.	Дата	Частный жилой дом	Стадия	Лист	Листов
		ГИП	Кухмар				12.20		Разрез 2-2	С	11
Инв.№ подл.		Разраб.	Кухмар				12.20	ИП Кухмар Д.А. Свидетельство о регистрации №192530011 Адресом соответствия ИЛС: №0001934-ГР, №0002091-ГР до 05.12.2021			
		Н.контр.	Кухмар				12.20				

3D-визуализация



Вид 1



Вид 2

Инв.№ подл.	Подп. и дата	Взаим.инв.№								
								Вид 2		
								Строительство жилого дома на земельном участке площадью 0,1479 га по адресу: Минский р-н, Колодищанский с/с, п. Колодищи, ул. Алеся Адамовича,		
		Изм.	Кол.ч.	Лист	Ндок.	Подп.	Дата			
ГИП	Кухмар				12.20	Частный жилой дом				
Разраб.	Кухмар				12.20					
						3D-визуализация. Вид 1. Вид 2				
Н.контр.	Кухмар				12.20	ИП Кухмар Д.А. Свидетельство о регистрации №192530011 Аттестаты соответствия ИЛС: №0001934-ГР, №0002091-ГР до 05.12.2021				