
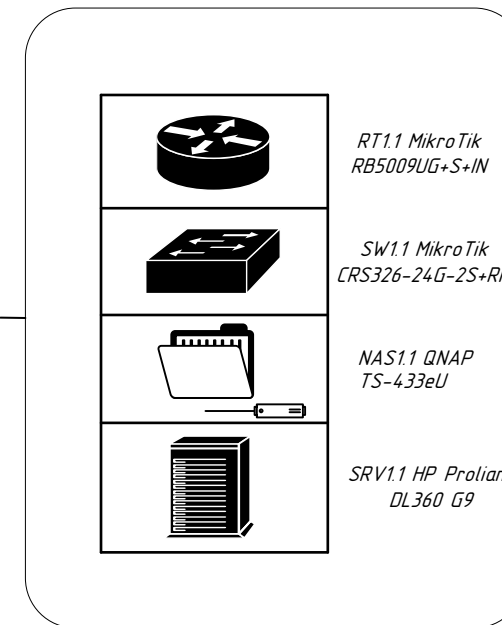


Первый этаж

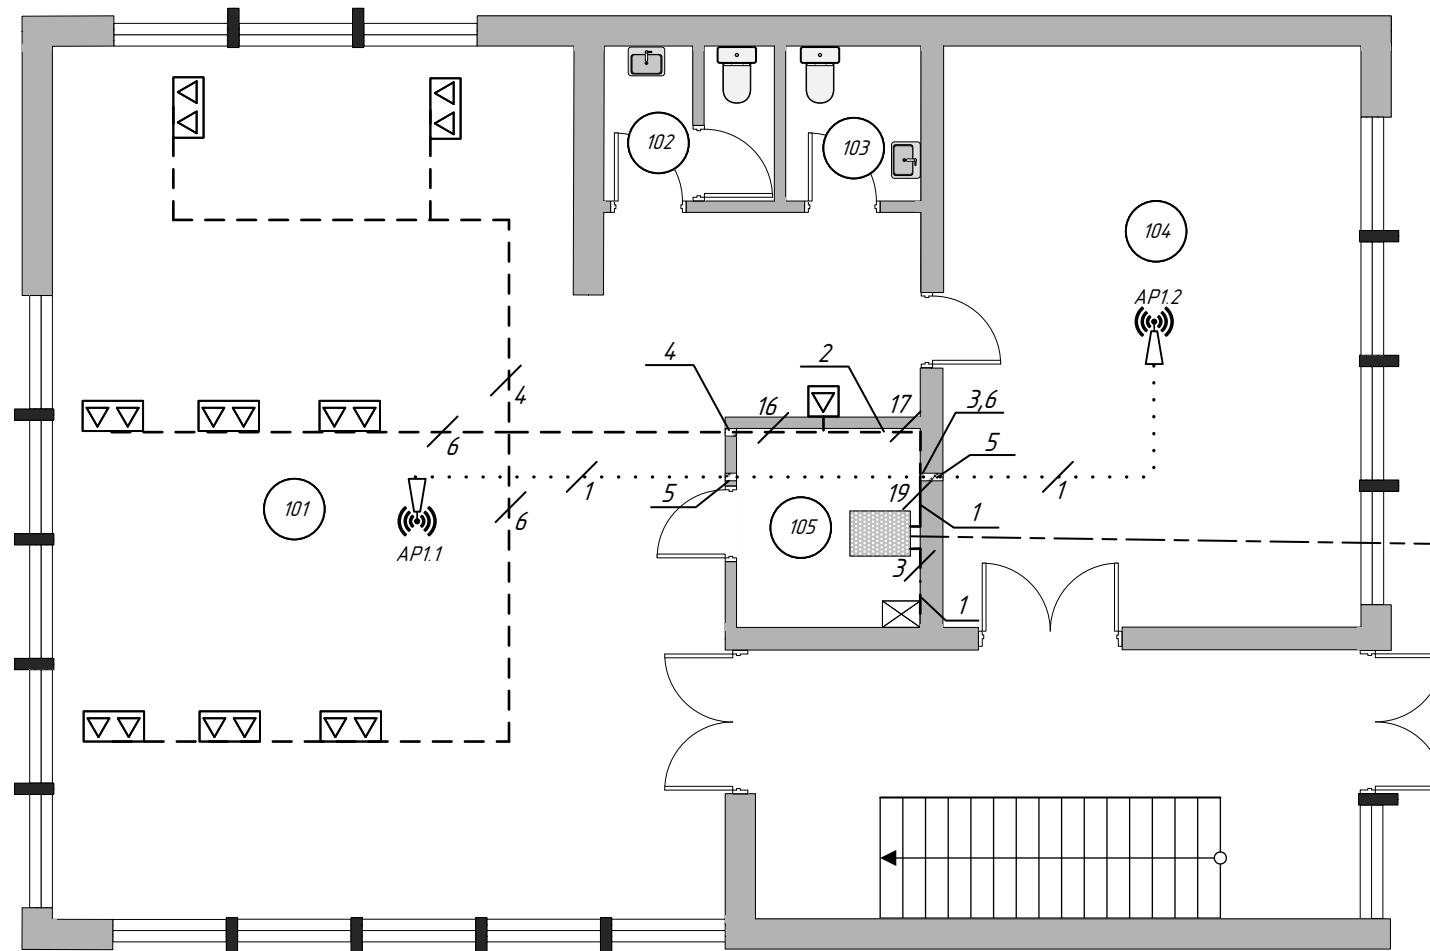

Технические требования:

Кабель прокладывается в кабель-канале под полом, над
фальшпотолком и вдоль стены на расстоянии 20 см от
пола.

Информационные розетки на всех этажах
располагаются в напольных люках.

Шкаф ставится на пол в серверной комнате.

Точки доступа монтируются к фальшпотолку. Необходимо использовать специальную металлическую монтажную пластину, которая устанавливается сверху плиты, а снизу к ней крепится пластина из комплекта точки доступа, для это просверлить отверстия для шурупов. Необходимо сделать отверстие в фальшпанели для кабеля, пропустить его через него, подключить к точке доступа, а затем зафиксировать ее на пластине.

1. Кабель располагается вдоль стены на расстоянии 20 см от пола.
2. Кабель располагается в полу.
3. Кабель располагается над фальшпотолком.
4. В данном месте кабель пускается в канал смонтированный под стеной.
5. В данном месте кабель пускается в канал смонтированный над фальшпотолком через стену.
6. Кабель опускается/поднимается вертикально по стене.

Условные обозначения



Информационная розетка RJ45 для стационарного подключения



Двойная информационная розетка RJ45
для стационарного подключения



Телекоммуникационный шкаф



Железобетонная стена



Кирпичная стена



Стальная балка



Панорамное
остекление




Кабельная шахта




Номер помещения




Беспроводная точка
доступа

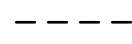

Витая пара в кабель
канале в полу

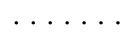


Витая пара в гофрированной
трубе над фальшпотолком

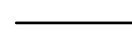

Витая пара в кабель канале



Два патч-корда Cat6, 15
метров + одно оптоволокно в
кабель канале

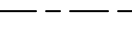

Комментарий

					ГУИР.400201.021 СЗ							
					Локальная компьютерная сеть. План здания	Лит.			Масса		Масштаб	
Изм.	Лист	N докум.	Подп.	Дата			У			1:100		
Разраб.		Николайчик										
Пров.		Глецевич										
						Лист 1			Листов 2			
						ЭВМ, зр. 250501						