

Технические требования:




Кабель везде прокладывается в кабель-канале вдоль стены на расстоянии 30 см от потолка.

Информационные розетки на всех этажах располагаются на высоте 50 см от уровня пола. Кабель опускается вертикально вниз в таких местах.


Шкаф крепится к стене на высоте 150 см от уровня пола.

Точки доступа монтируются к потолку.

- 1) Переход между этажами.
- 2) Кабель поднимается вверх вдоль стены на расстояние 30 см от потолка.
- 3) В данном месте для дальнейшей прокладки кабеля сверлится отверстие в стене и через него проводится кабель.
- 4) Кабель проводится над фальшь-потолком.

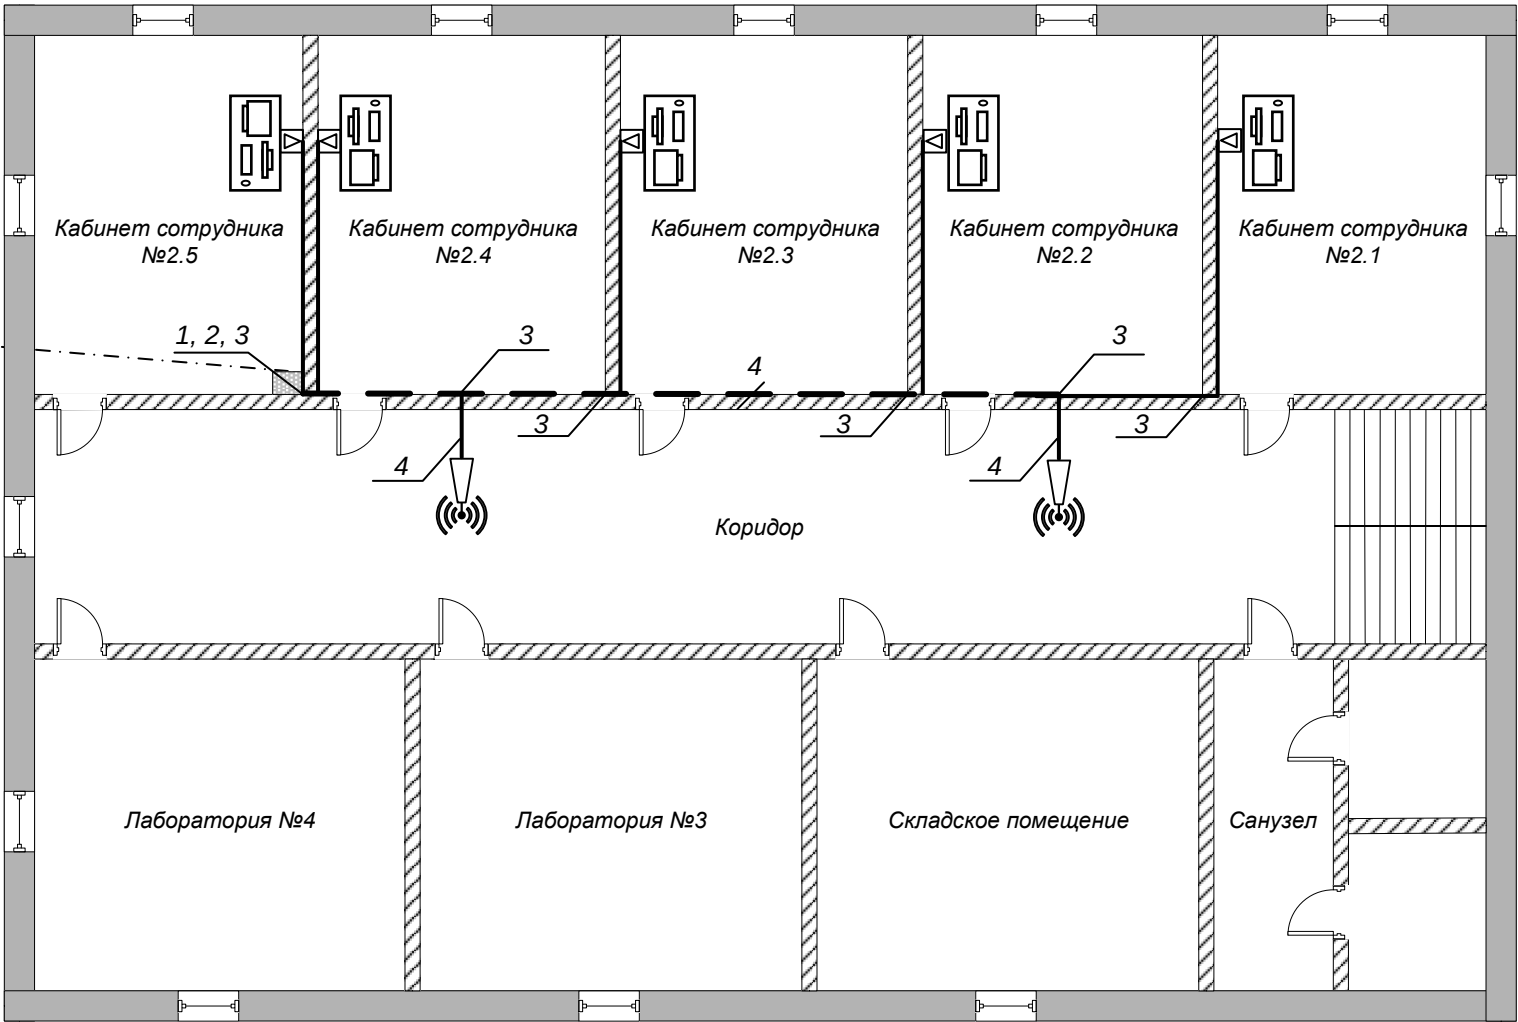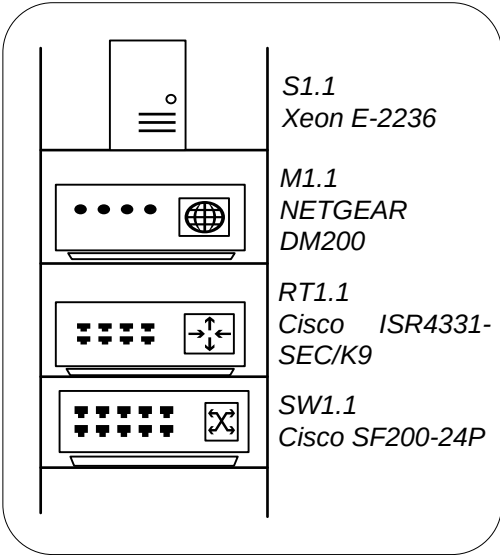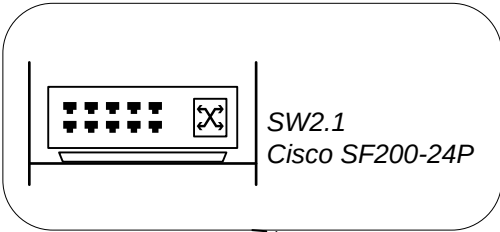

Первый этаж

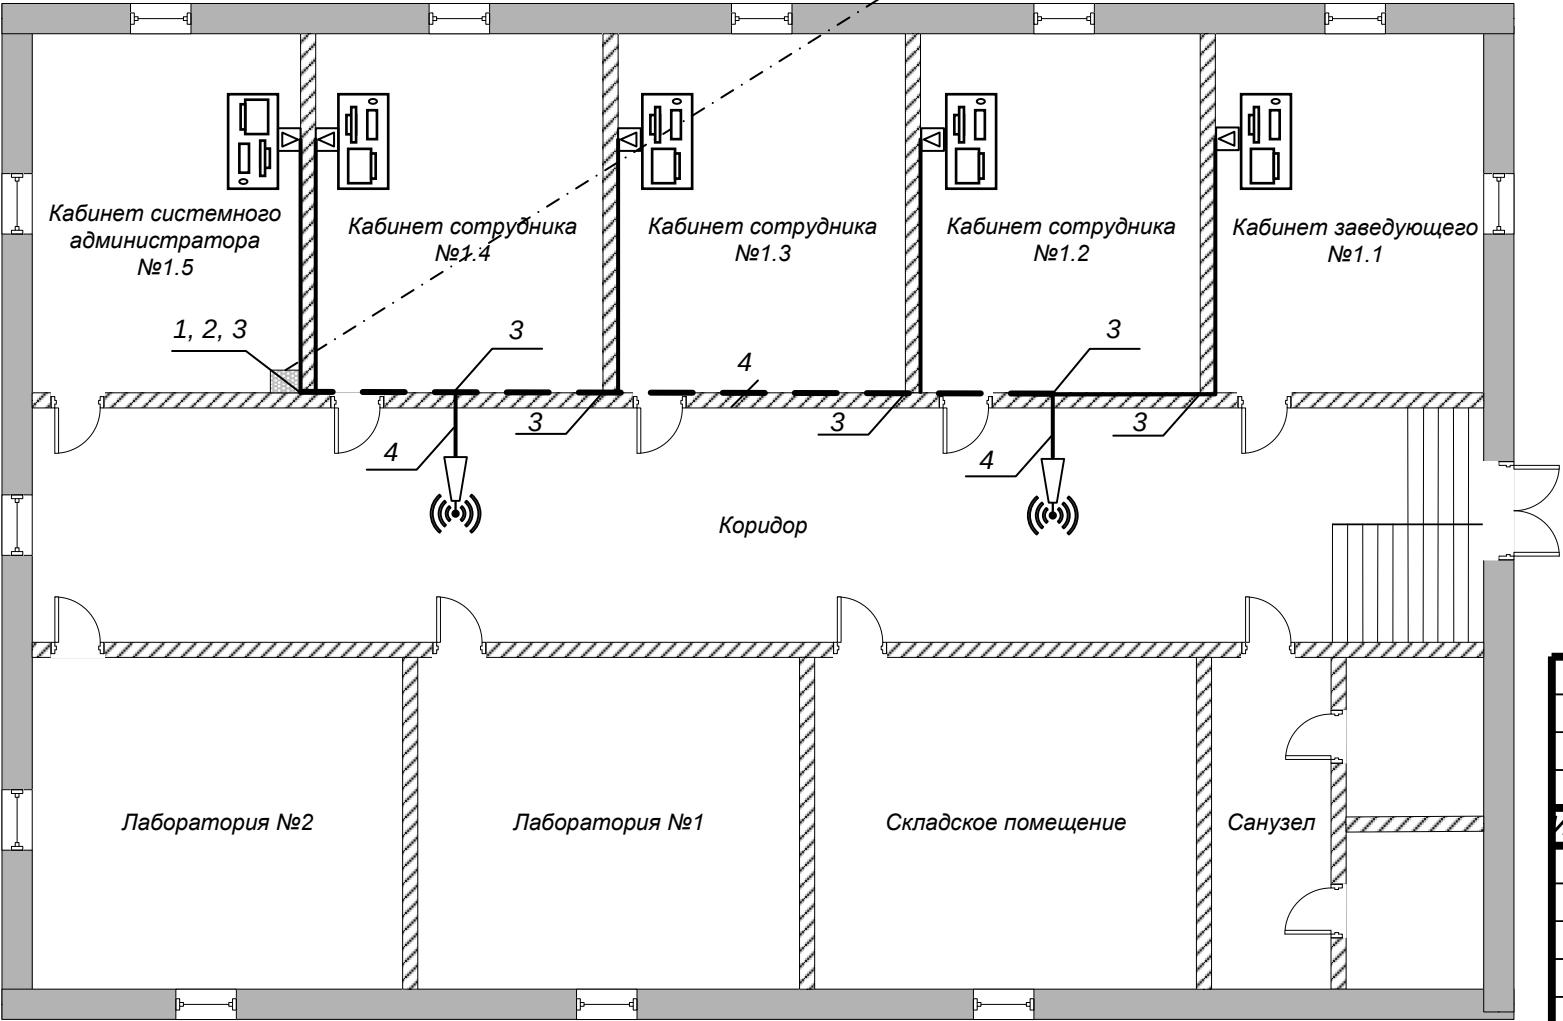

Второй этаж

Условные обозначения:

	DSL-модем		Web-сервер		Информационная розетка
	Маршрутизатор		Беспроводная точка доступа WAP150		Многофункциональное устройство
	Коммутатор		Комментарий		Стационарное рабочее место
	Телекоммуникационный шкаф настенный TC6401-06G		Витая пара в кабель-канале 11x10		Железобетонная стена
			Витая пара в кабель-канале 24x22		Газосиликатная стена

					ГУИР.400201.024 С3				
					Локальная компьютерная сеть. План здания	Лит.		Масса	Масштаб
Изм.	Лист	№ докум.	Подп.	Дата			у		1:125
Разраб.		Шаповалова							
Пров.		Глецевич							
					Лист 1		Листов 1		
					ЭВМ, гр. 150501				